


NOTAS:

1 - PROJEÇÃO DA REDE PRIMÁRIA COM POSTEAMENTO E TRANSFORMADORES É SOMENTE ORIENTATIVO/PREVISTO, DEVERÁ SER REALIZADO ESTUDO PELA ELEKTRO PARA ATENDER OS GRUPOS DE MEDIDAS OU O CLIENTE OPTAR POR EXECUÇÃO POR TERCEIROS(EMPRESA CADASTRADA) COM APRESENTAÇÃO DE PROJETO ESPECÍFICO.

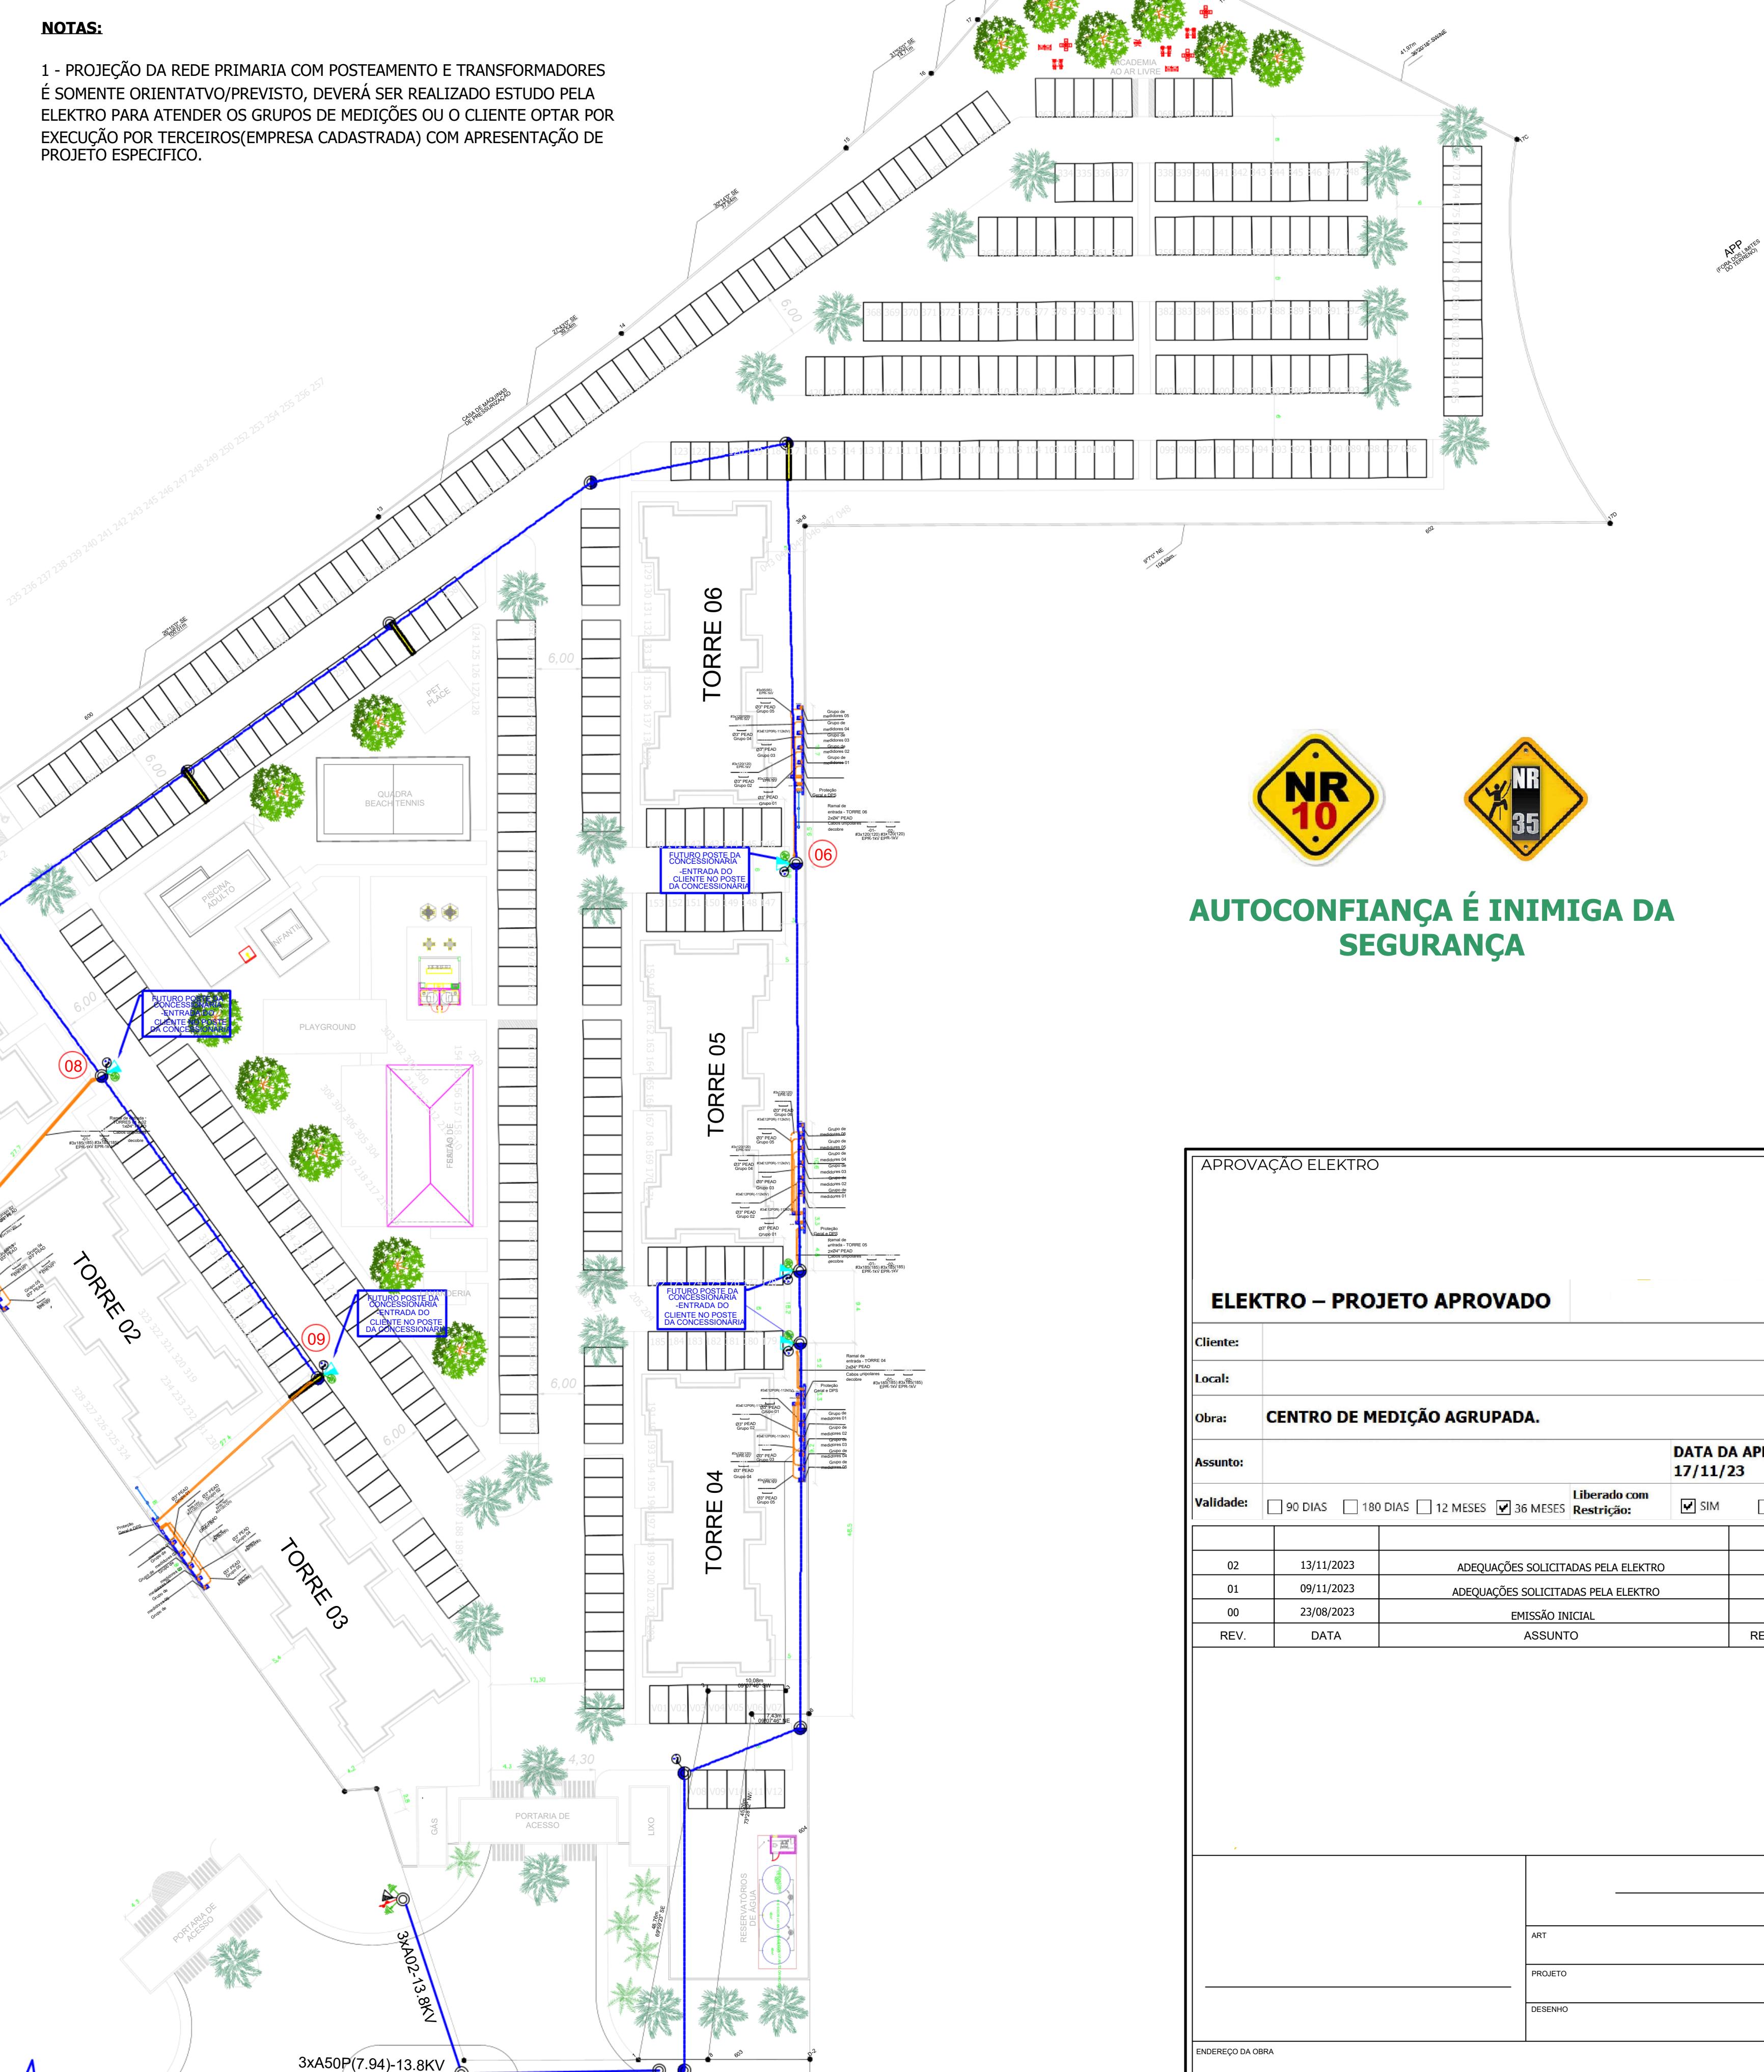

AUTOCONFIANÇA É INIMIGA DA SEGURANÇA

APROVAÇÃO ELEKTRO

ELEKTRO – PROJETO APROVADO

Cliente:			
Local:			
Obra:	CENTRO DE MEDAÇÃO AGRUPADA.		
Assunto:			DATA DA APROVAÇÃO: 17/11/23
Validade:	<input type="checkbox"/> 90 DIAS <input type="checkbox"/> 180 DIAS <input type="checkbox"/> 12 MESES <input checked="" type="checkbox"/> 36 MESES	Liberado com Restrição:	<input checked="" type="checkbox"/> SIM <input type="checkbox"/> NÃO
02	13/11/2023	ADEQUAÇÕES SOLICITADAS PELA ELEKTRO	
01	09/11/2023	ADEQUAÇÕES SOLICITADAS PELA ELEKTRO	
00	23/08/2023	EMISSÃO INICIAL	
REV.	DATA	ASSUNTO	RESPONSÁVEL

		ART	
		PROJETO	
		DESENHO	
ENDERECO DA OBRA			
DESCRICAÇÃO DA OBRA			
CAIXA DE PROTEÇÃO GERAL E GRUPO DE MEDAÇÕES COLETIVAS			
TÍTULO			
PLANTA DE INSTALAÇÃO			
DATA	ESCALA	DESENHO NÚMERO	FOLHA
23/08/23	INDICADAS	N-24/23	1/5