


NOTAS:

1 - PROJEÇÃO DA REDE PRIMÁRIA COM POSTEAMENTO E TRANSFORMADORES É SOMENTE ORIENTATIVO/PREVISTO, DEVERÁ SER REALIZADO ESTUDO PELA ELEKTRO PARA ATENDER OS GRUPOS DE MEDIÇÕES OU O CLIENTE OPTAR POR EXECUÇÃO POR TERCEIROS(EMPRESA CADASTRADA) COM APRESENTAÇÃO DE PROJETO ESPECÍFICO.

PLANEJE
COORDENE
EXECUTE
COM
SEGURANÇA

NÃO CONFIE
TESTE
ATERRE
SINALIZE

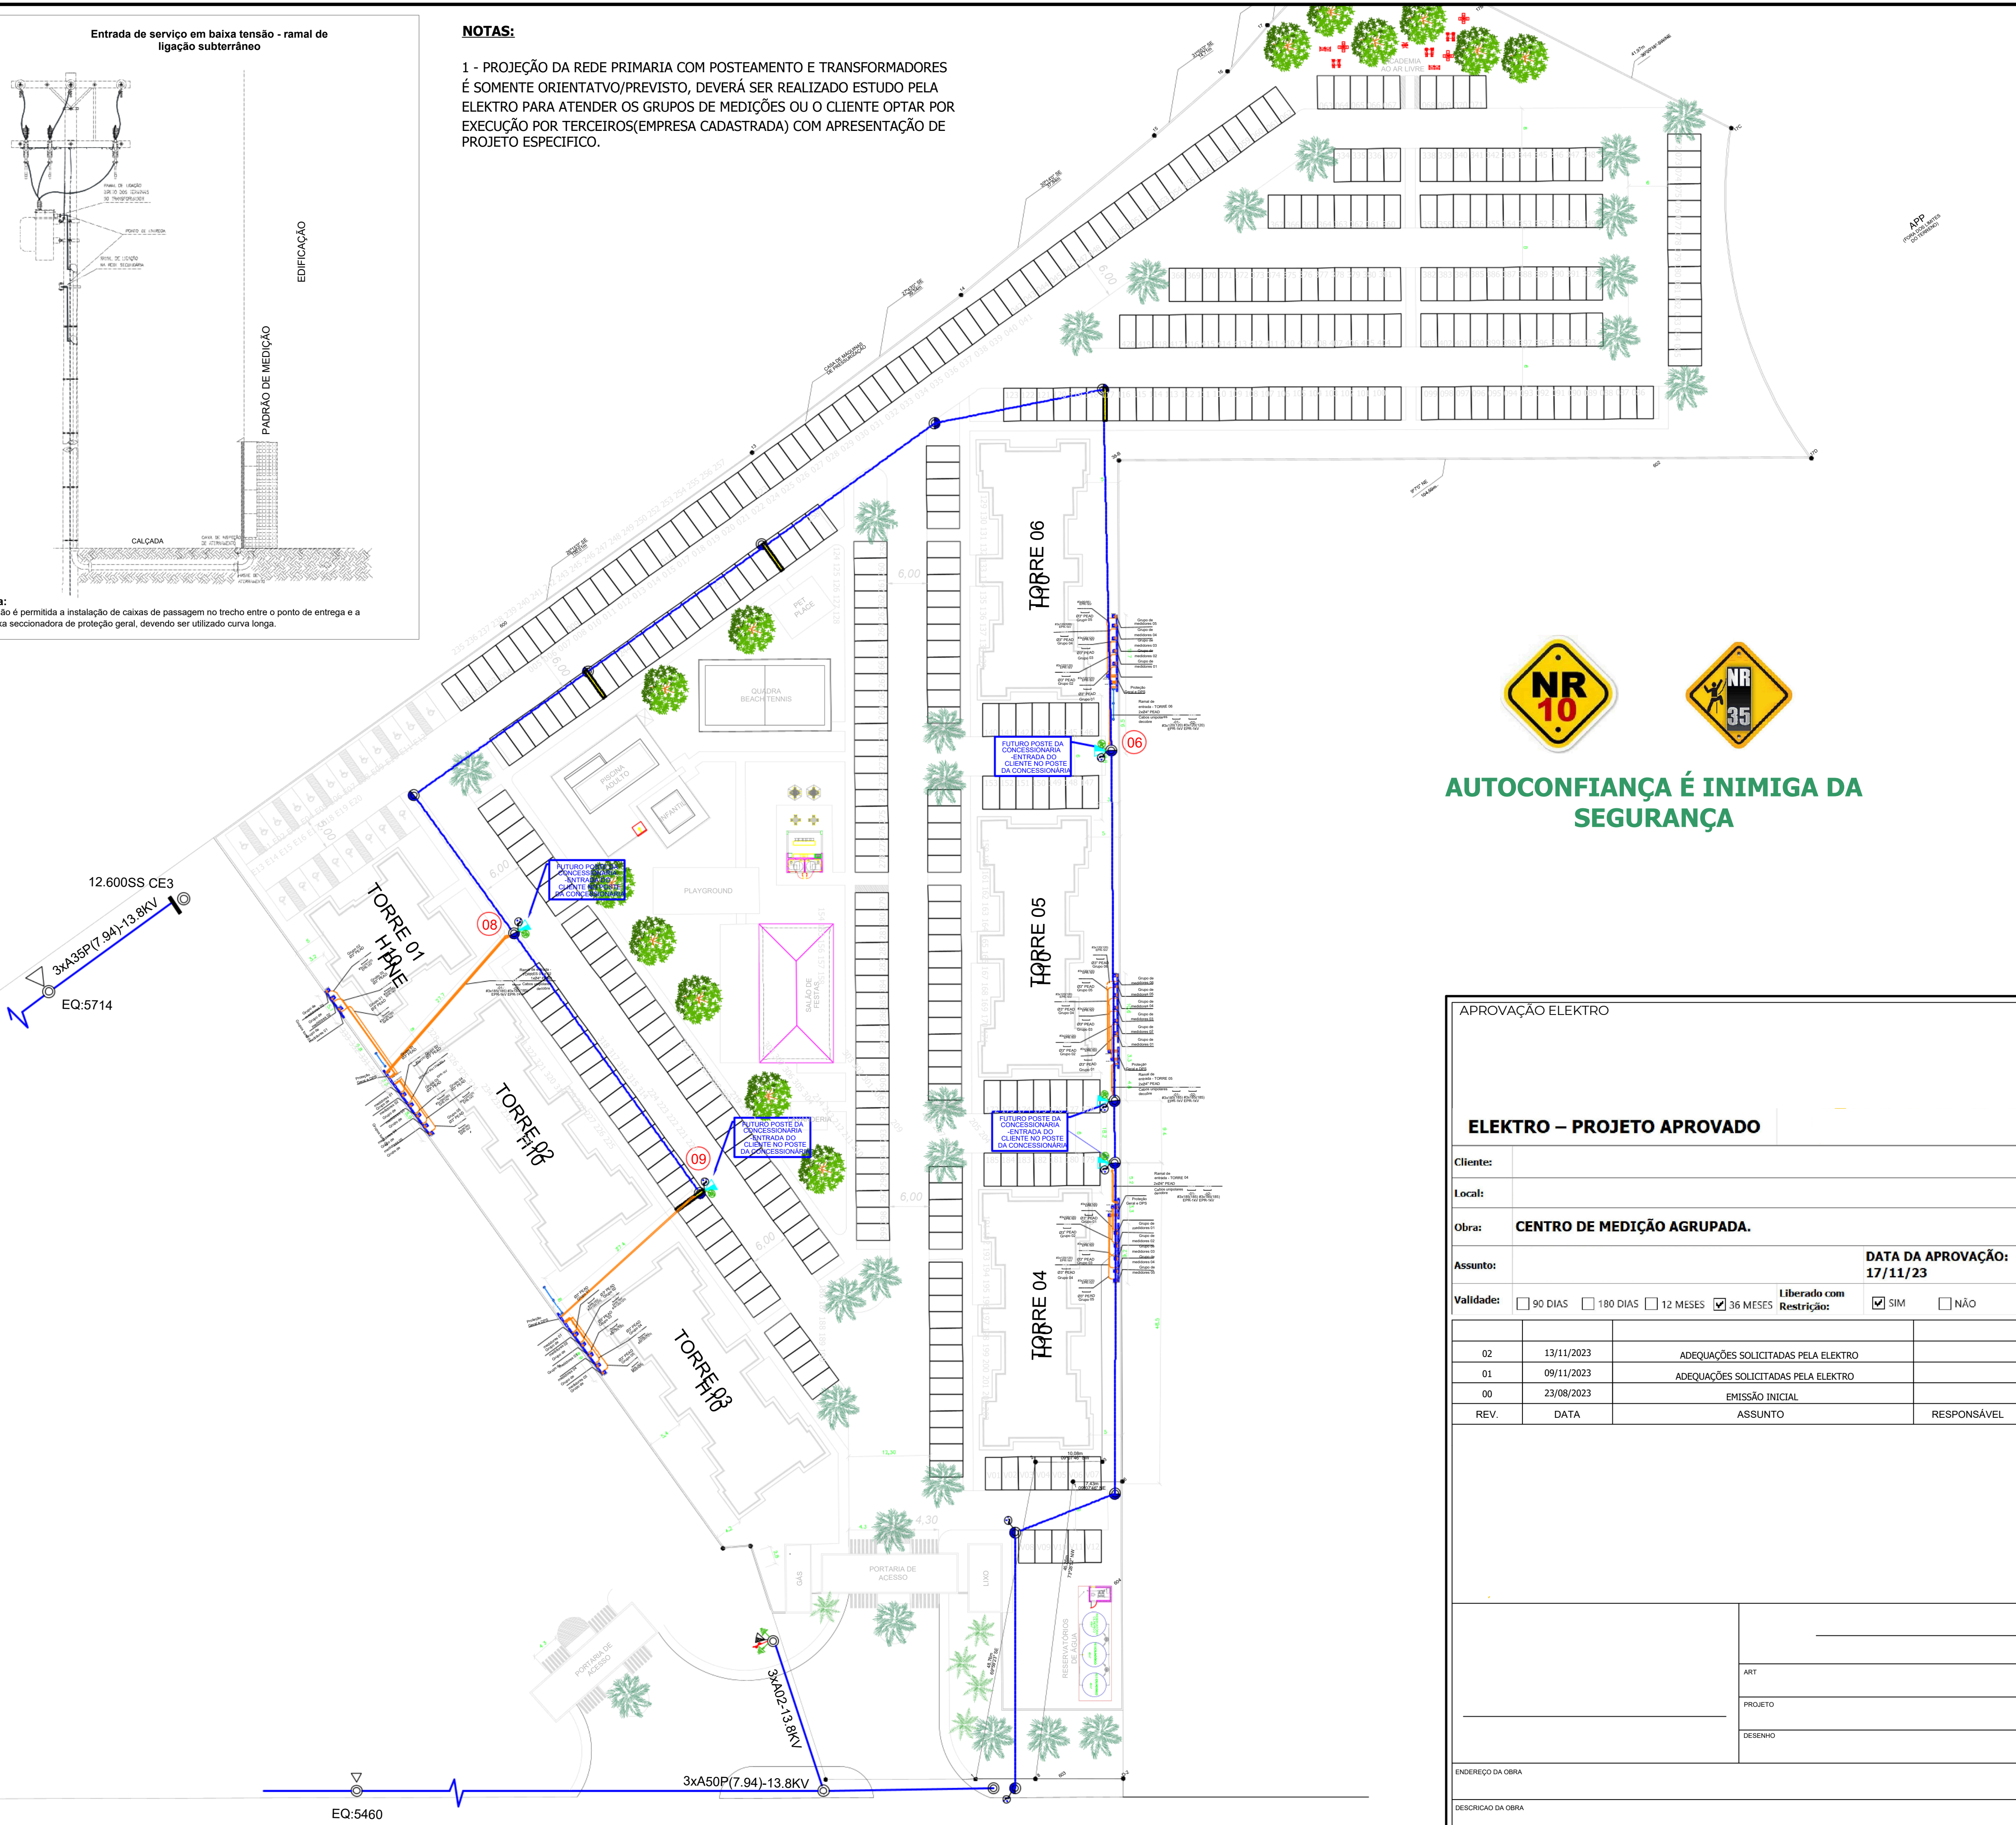

NR 10

NR 35

AUTOCONFIANÇA É INIMIGA DA SEGURANÇA

APROVAÇÃO ELEKTRO

ELEKTRO – PROJETO APROVADO

Cliente:			
Local:			
Obra:	CENTRO DE MEDIÇÃO AGRUPADA.		
Assunto:			DATA DA APROVAÇÃO: 17/11/23
Validade:	<input type="checkbox"/> 90 DIAS <input type="checkbox"/> 180 DIAS <input type="checkbox"/> 12 MESES <input checked="" type="checkbox"/> 36 MESES		<div>Liberado com Restrição:</div> <div><input checked="" type="checkbox"/> SIM <input type="checkbox"/> NÃO</div>
02	13/11/2023	ADEQUAÇÕES SOLICITADAS PELA ELEKTRO	
01	09/11/2023	ADEQUAÇÕES SOLICITADAS PELA ELEKTRO	
00	23/08/2023	EMIÇÃO INICIAL	
REV.	DATA	ASSUNTO	RESPONSÁVEL

ENDEREÇO DA OBRA	
DESCRICAÇÃO DA OBRA	
TÍTULO	CAIXA DE PROTEÇÃO GERAL E GRUPO DE MEDIÇÕES COLETIVAS
DATA	23/08/23
ESCALA	INDICADAS
DESENHO NÚMERO	N-24/23
FOLHA	1/5